SKYCAB WALL BEND-LINE TEMPLATES (C1, C2, C3, C4)

1. Print at 100% / "Actual size" (no "fit to page"). On every page the black bar must measure 5.0 cm.

2. Each piece is on 2 pages. Overlap them so the two grey JOIN lines sit exactly on top of each other; tape.

3. Push a pin through every red dot (each red line has a dot at the top and a dot at the bottom).

4. Lay the template FACE UP on your cardboard piece, wherever the outline fits exactly:
   - normal piece: on the PAPER side - FLIPPED COPY: on the BARE BACK
   Line it up by the dashed fold lines (the V-notch tips) and the two end edges.

5. Pencil a dot through every pin hole. Lift the template.
   If you marked the paper side: push the pin through the cardboard at each dot, so the dots show on the back.

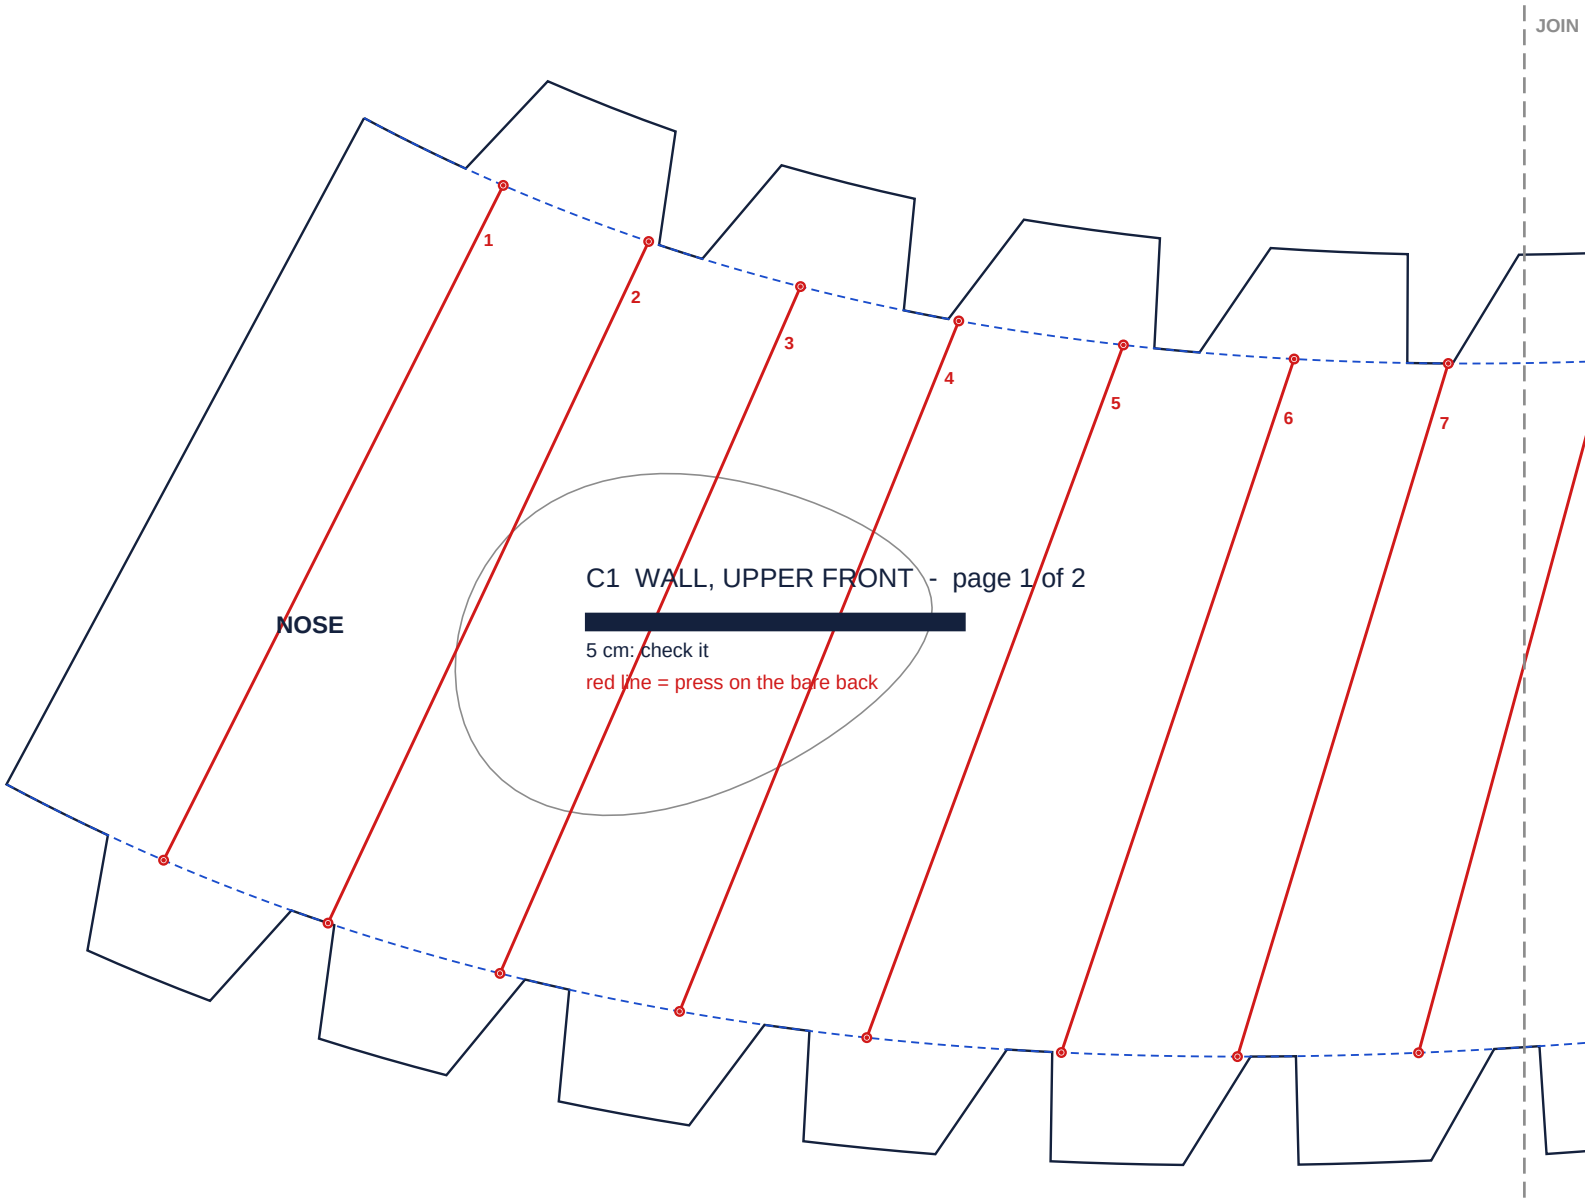
6. On the BARE BACK, join each top dot to its bottom dot with the ruler (they go in order: 1st with 1st, 2nd with 2nd...). Press each line hard with a butter knife or empty ballpoint. Do NOT cut.

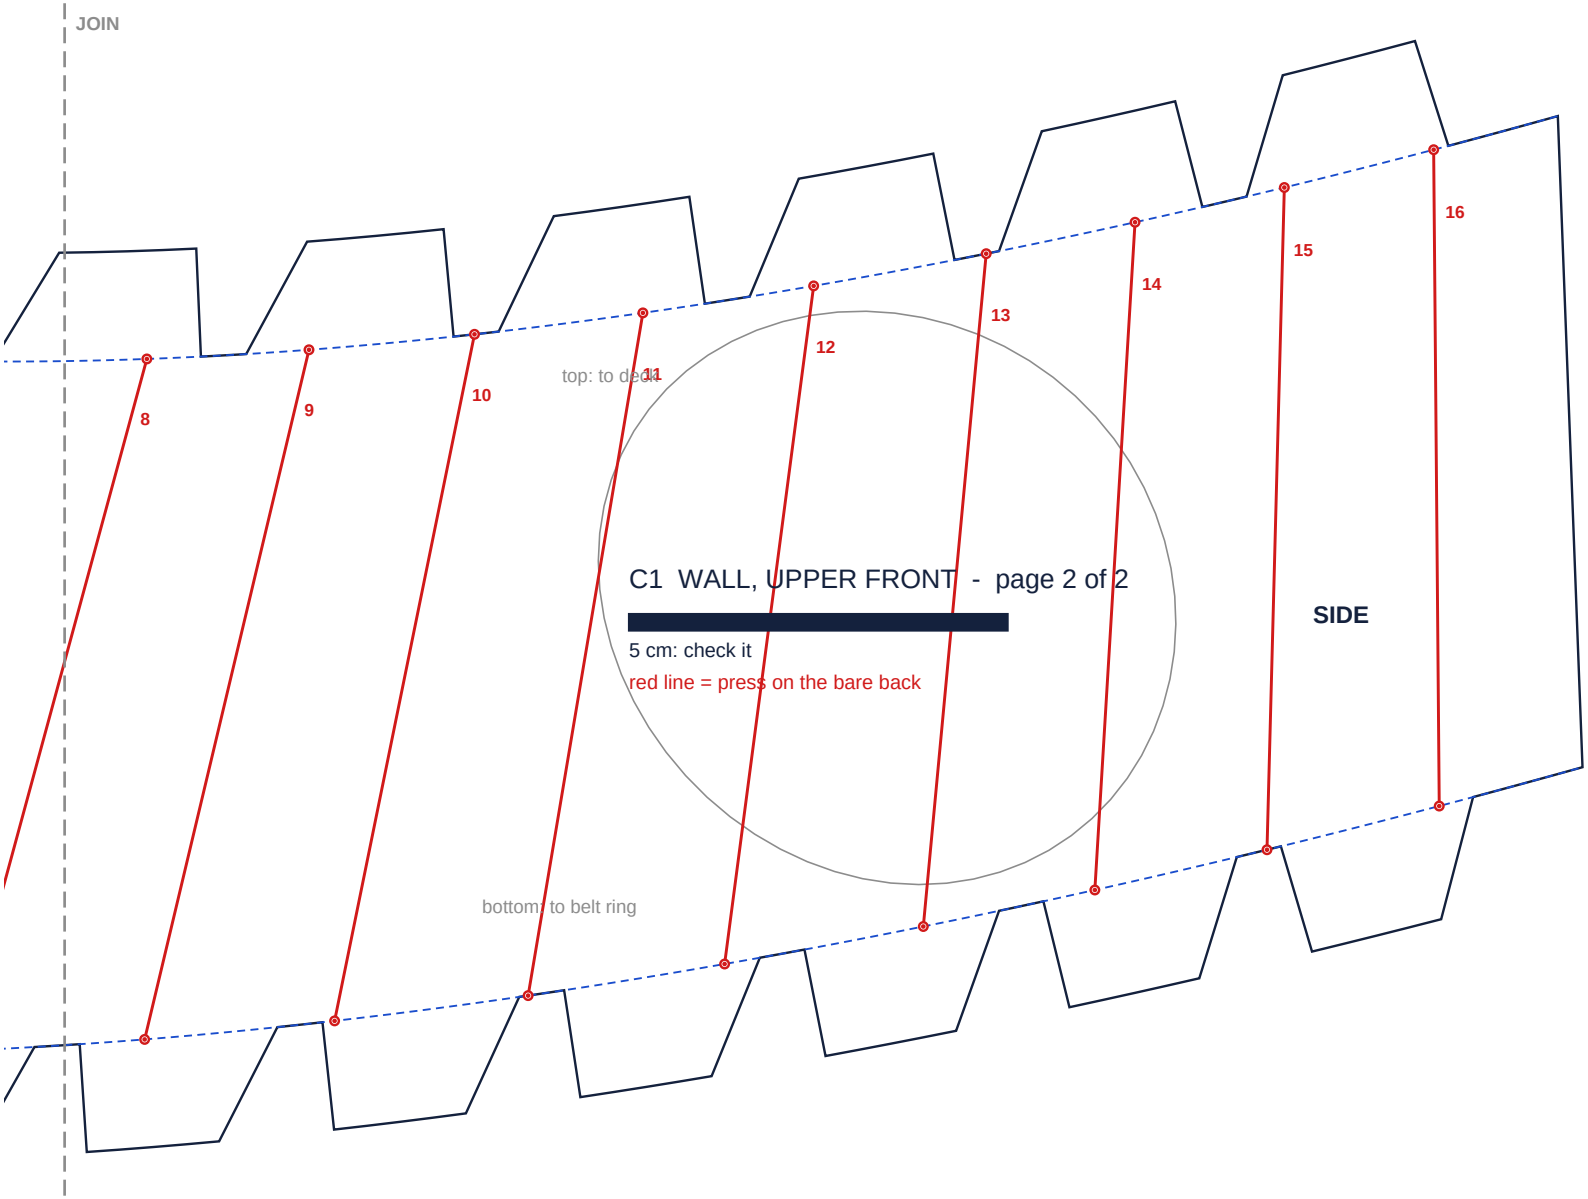
7. Bend a little at every line, paper side out, like slowly closing a fan. Then glue tab by tab (upper walls: from the NOSE along the deck; lower walls: along the belt ring) and let the edge pull it round.

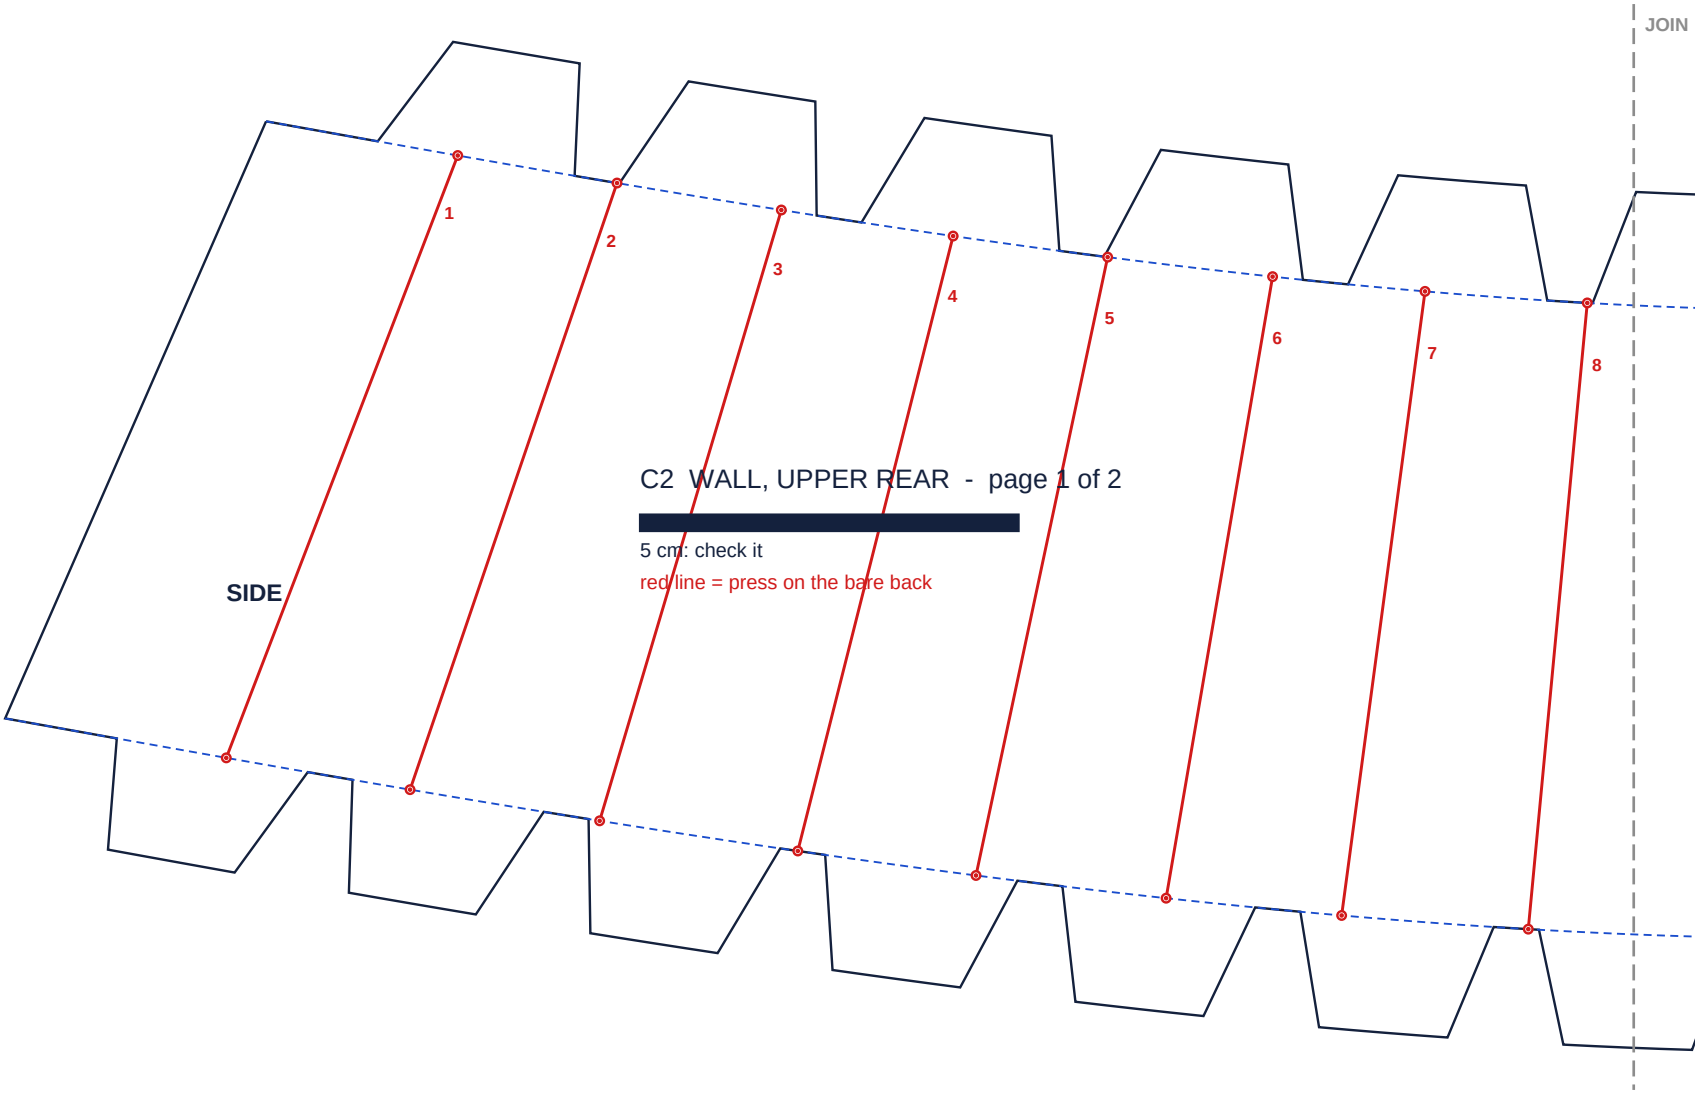
Why: the pieces fan out, so towards one end the bend runs up to 25 degrees across the tubes. Pressed lines make it bend in small neat steps there instead of snapping a tube.

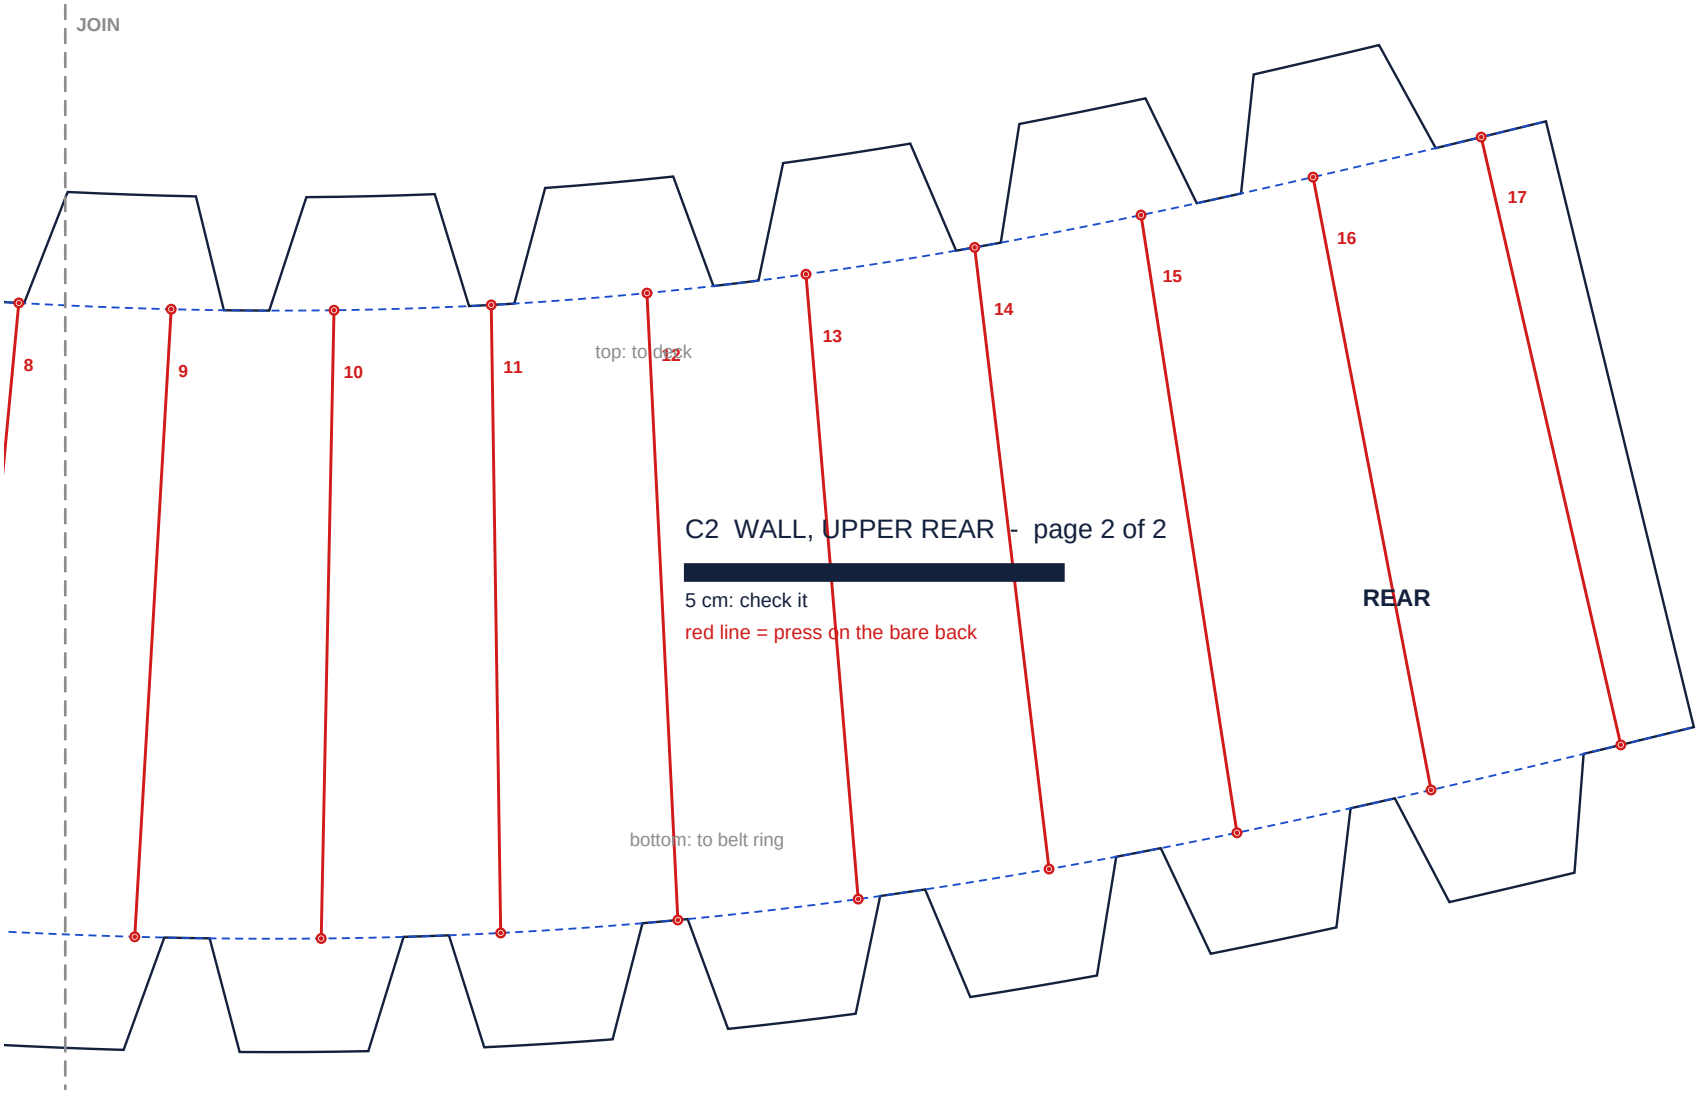
A tube already snapped? Leave it. The lines either side share the bend; paper and paint hide it.
A spot still fighting? Run the knife lightly along that line on the BARE BACK, through the top skin only, never through to the paper side.

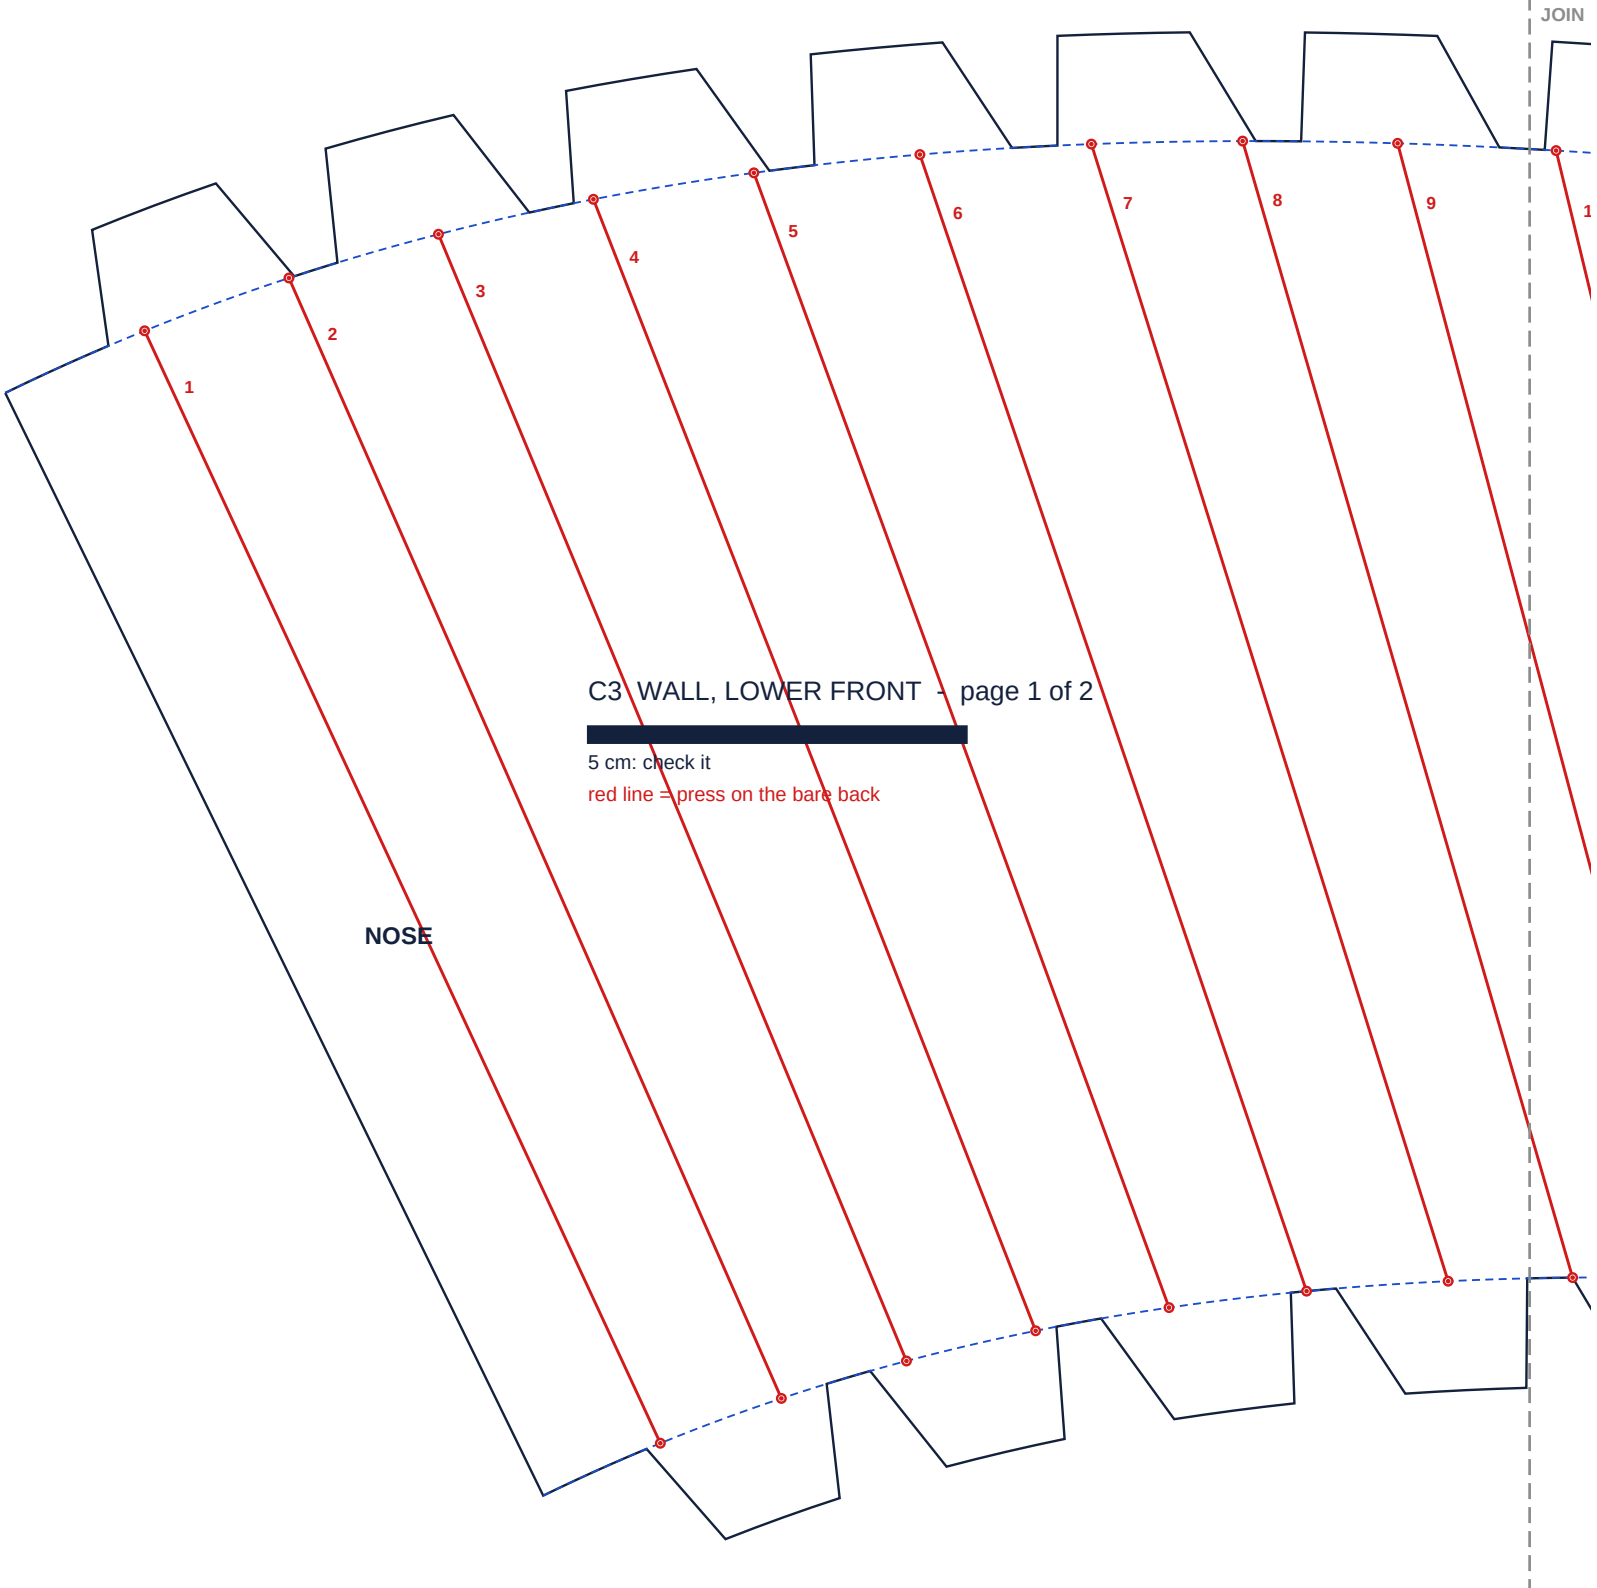
Same lines as the green press lines on the 36 inch roll corrections page: use whichever print you have.

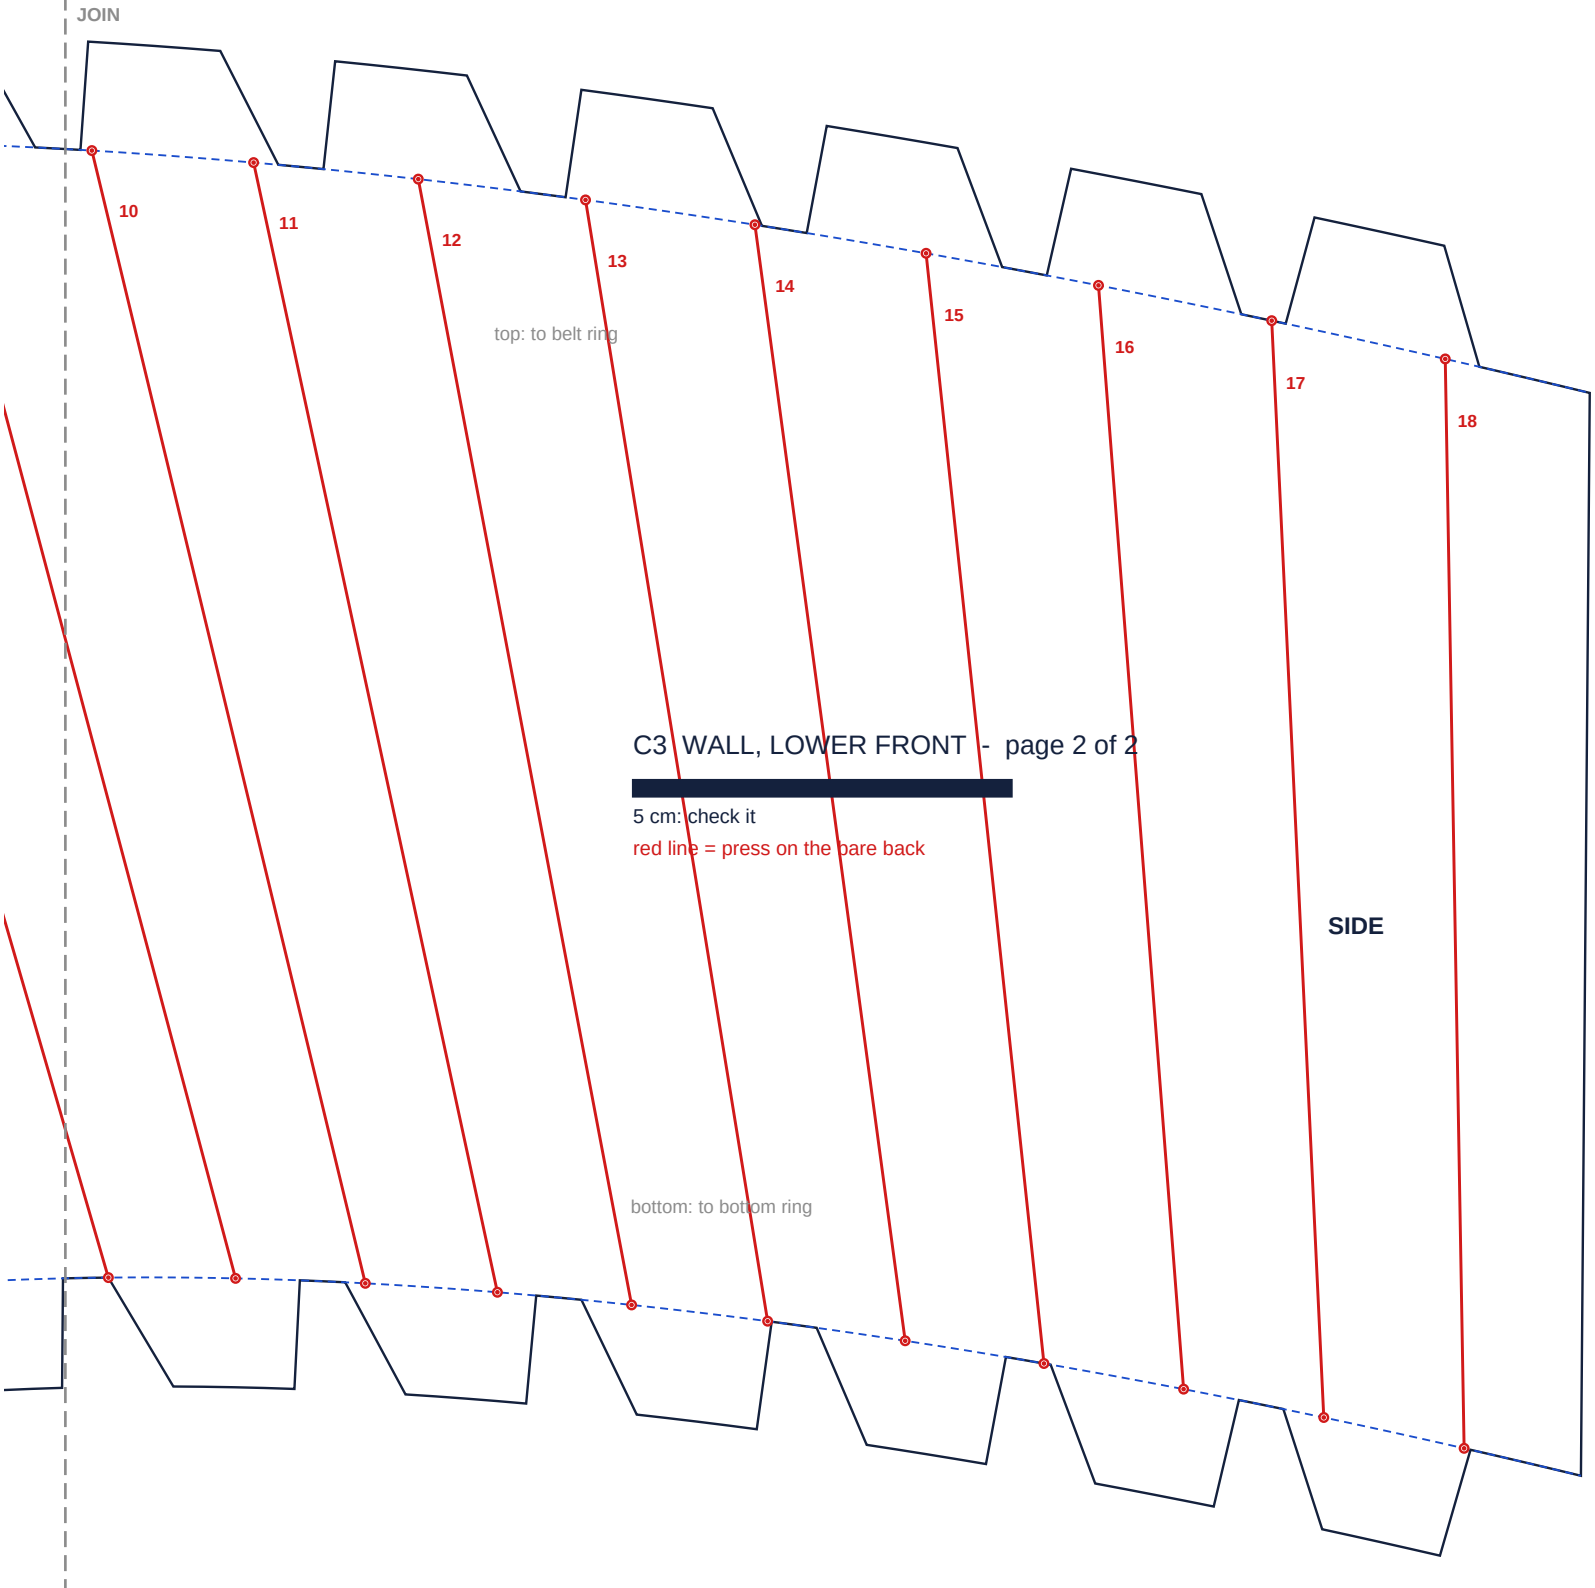

JOIN
1
2
3
4
5
6
7
NOSE
C1 WALL, UPPER FRONT - page 1 of 2
5 cm: check it
red line = press on the bare back

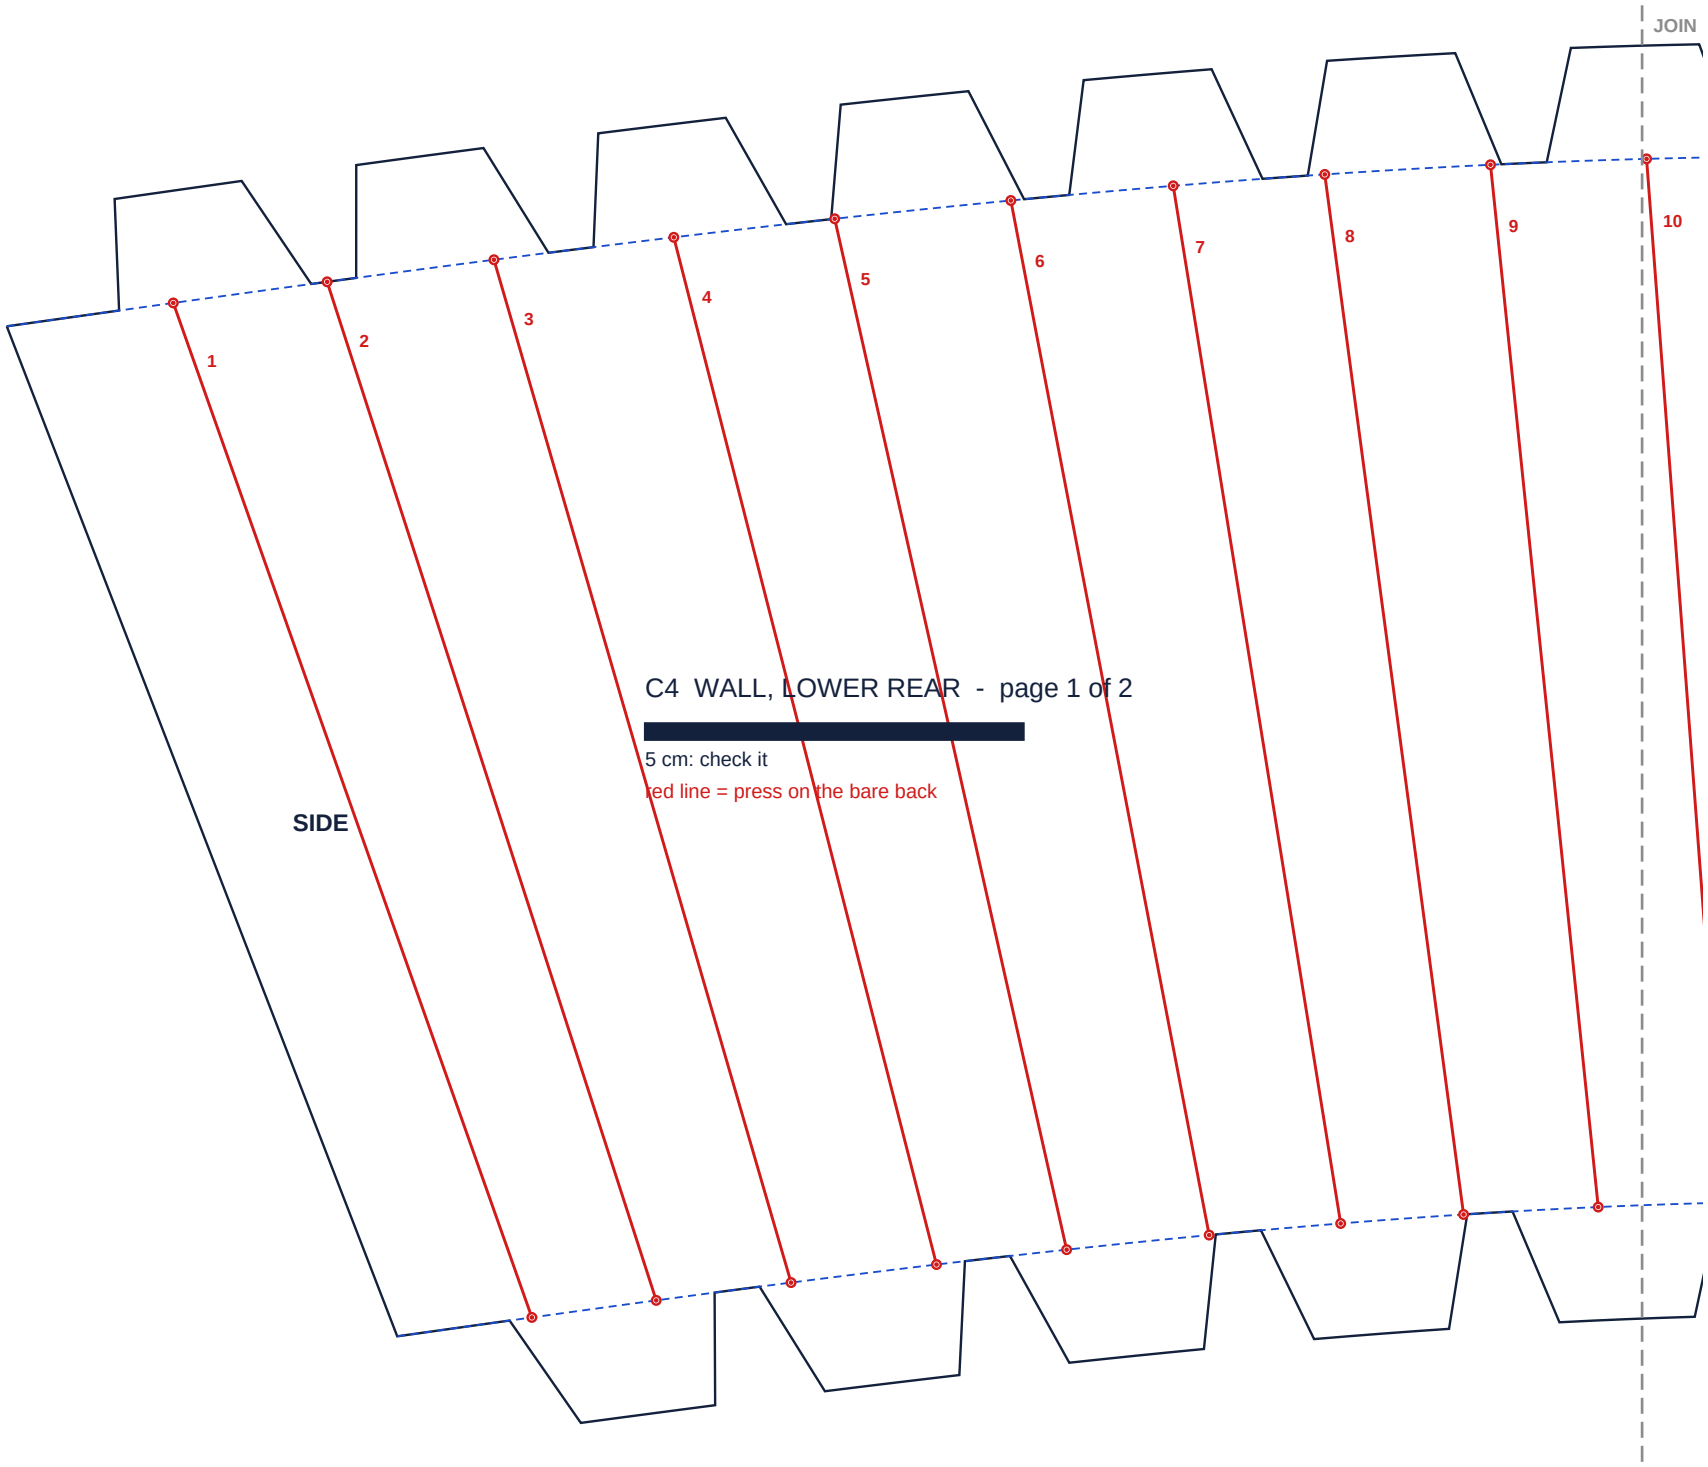

JOIN
top: to dart
bottom: to belt ring
8
9
10
11
12
13
14
15
16
C1 WALL, UPPER FRONT - page 2 of 2
5 cm: check it
red line = press on the bare back
SIDE


JOIN
1
2
3
4
5
6
7
8
SIDE
C2 WALL, UPPER REAR - page 1 of 2
5 cm: check it
red line = press on the bare back


JOIN
8
9
10
11
12
13
14
15
16
17
top: to desk
bottom: to belt ring
C2 WALL, UPPER REAR - page 2 of 2
5 cm: check it
red line = press on the bare back
REAR


JOIN
1
2
3
4
5
6
7
8
9
C3 WALL, LOWER FRONT - page 1 of 2
5 cm: check it
red line = press on the bare back
NOSE

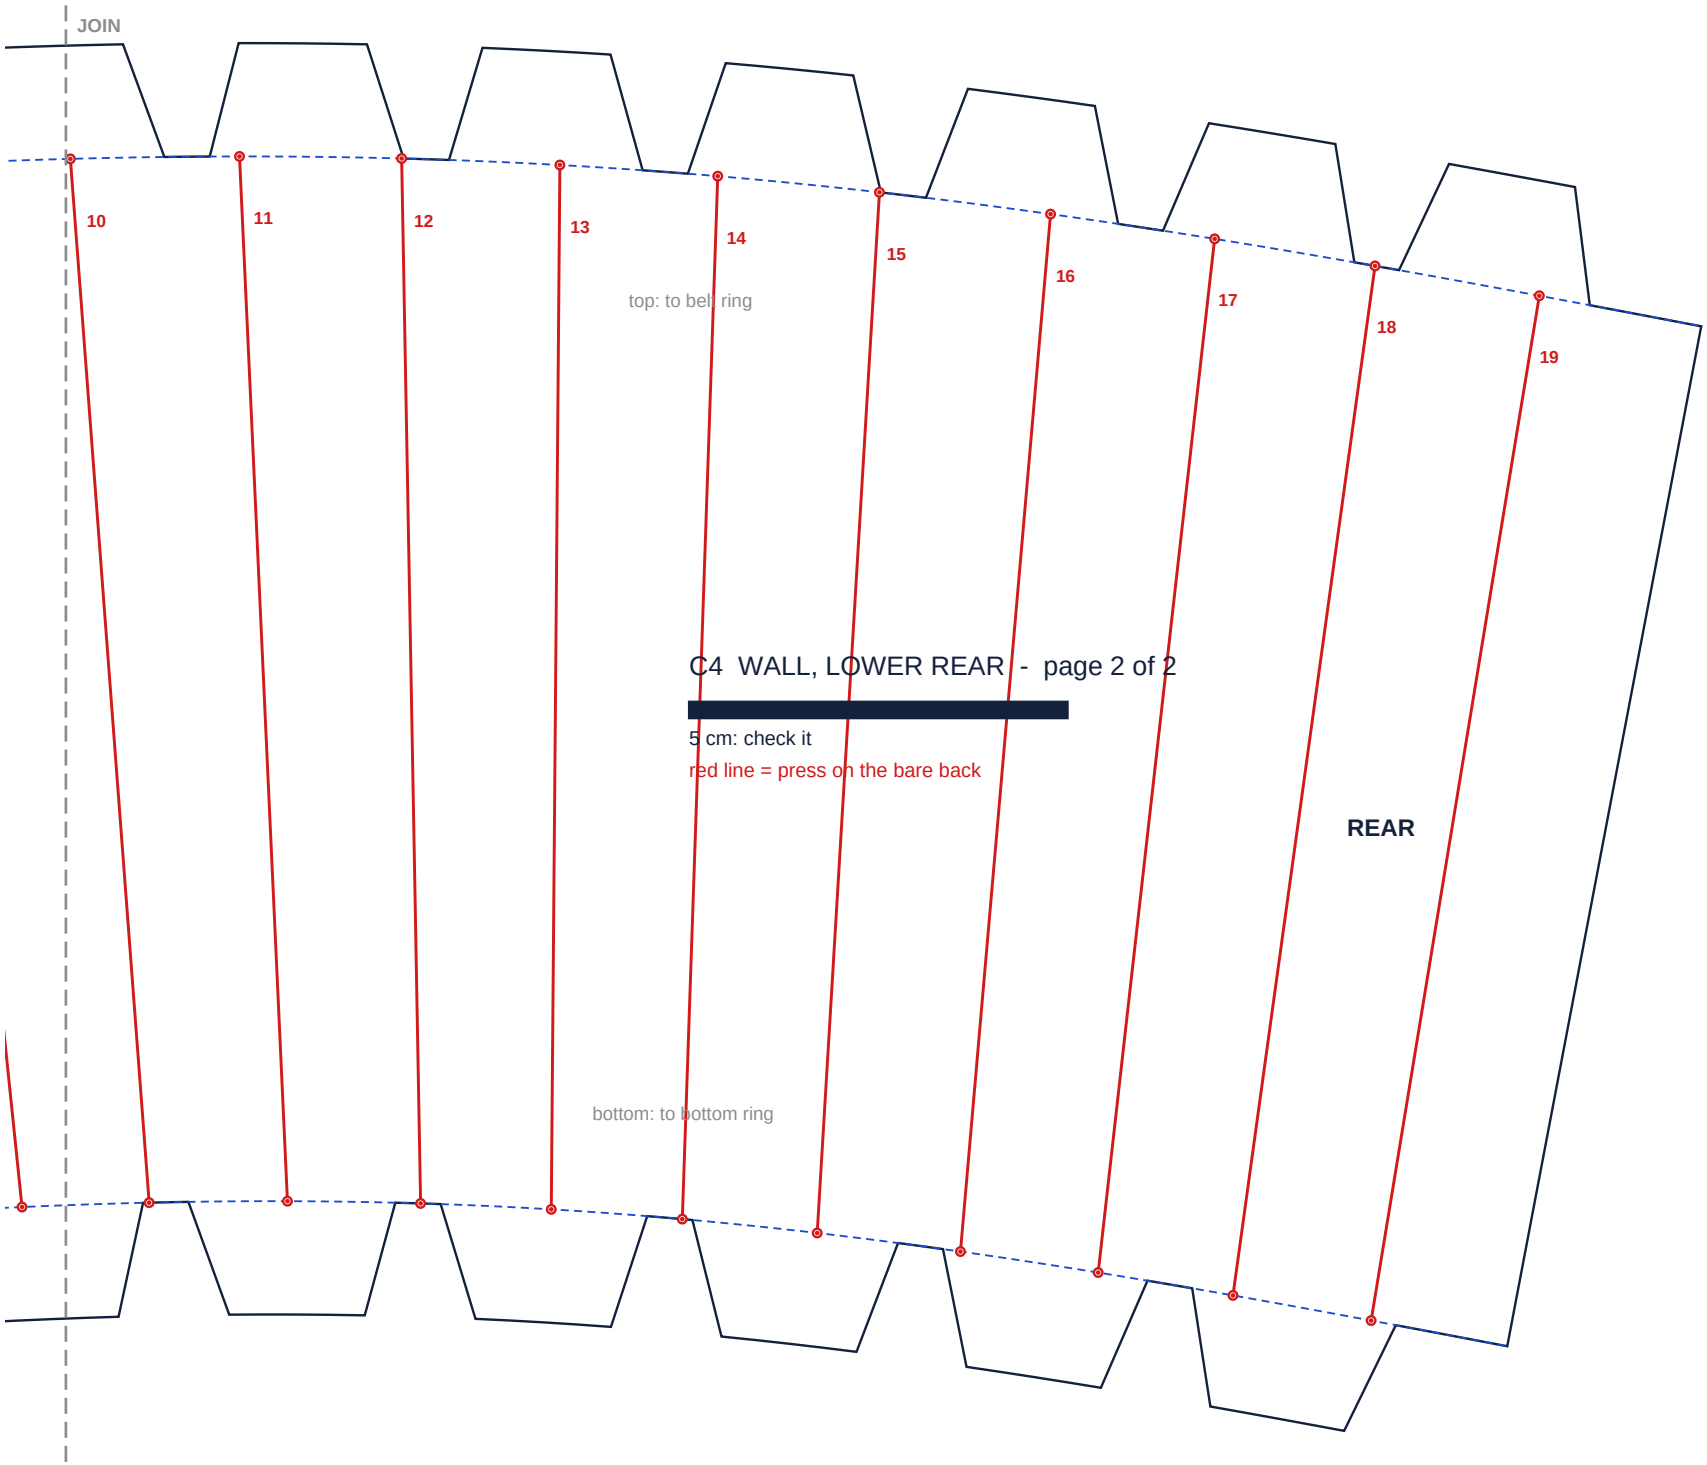

JOIN
10
11
12
13
14
15
16
17
18
top: to belt ring
C3 WALL, LOWER FRONT - page 2 of 2
5 cm: check it
red line = press on the bare back
SIDE
bottom: to bottom ring



C4 WALL, LOWER REAR - page 1 of 2

5 cm: check it

red line = press on the bare back


JOIN
10
11
12
13
14
15
16
17
18
19
top: to belt ring
C4 WALL, LOWER REAR - page 2 of 2
5 cm: check it
red line = press on the bare back
REAR
bottom: to bottom ring